Glazing

	Description	Quantity
W-1	W-1	4
W-2	W-2	5
W-3	W-3	7

Flooring

Carpet 1	1,823	sf
Carpet 2	4,526	sf
Carpet 3	782	sf
Hardwood	720	sf
Tile	1,399	sf
Type A Coating	3,488	sf

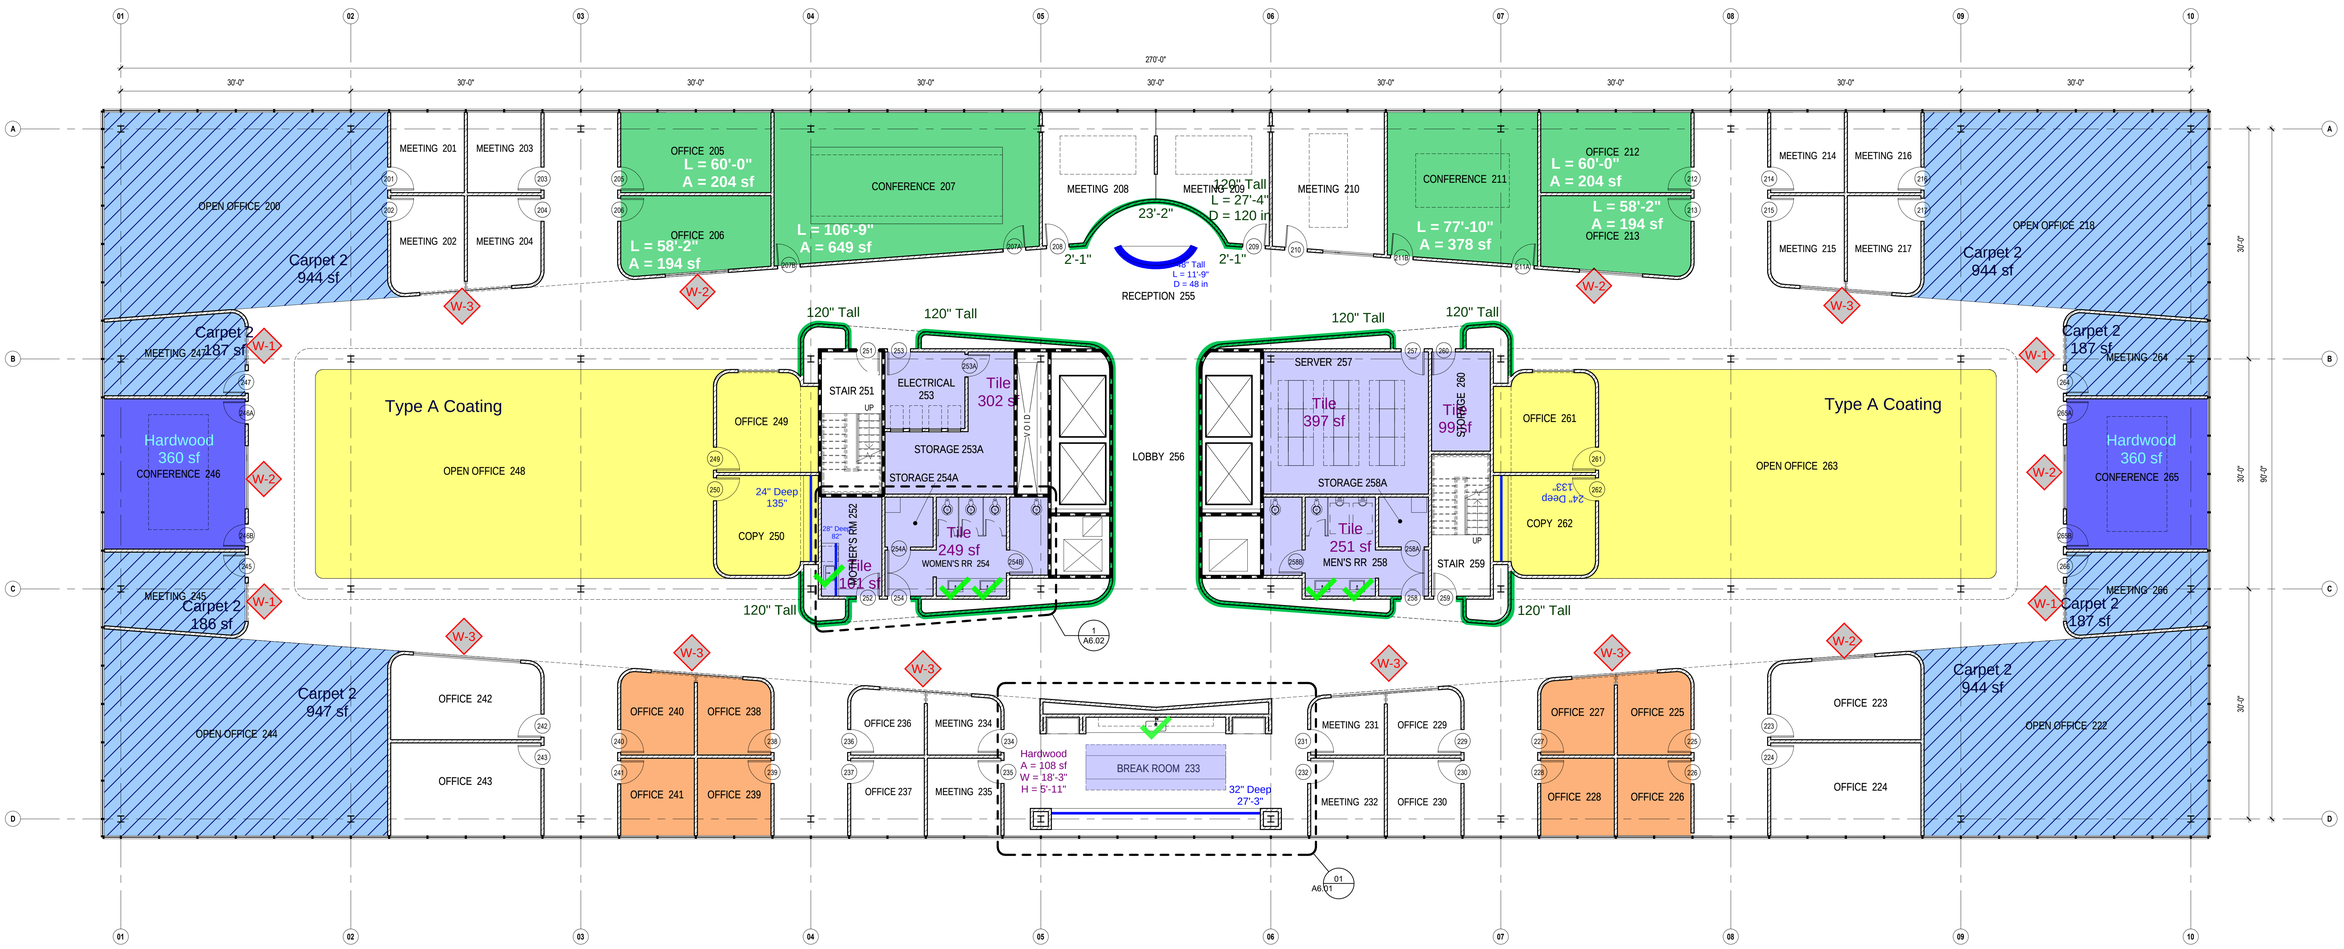

BLUEBEAM®
A NEMETSCHEK COMPANY

CAPTURE ENGINEERS
Mechanical
Electrical
Plumbing

1234 Miller St.
Manchester, NH 06930

REVU ARCHITECTS

5555 N. Broad St
Pasadena CA 91101

OFFICE BUILDING

Project No: 323232

Project Address:
123 Schonsett St
Chicago, IL 60601

THIS DRAWING IS INTENDED FOR DEMONSTRATION PURPOSES ONLY. DO NOT USE THIS DRAWING FOR ANY OTHER PURPOSE WITHOUT THE EXPRESS WRITTEN PERMISSION OF BLUEBEAM, INC.

DATE	03/04/2018
ISSUED FOR:	INTERNAL REVIEW
PROJECT	3232
DRAWN BY:	Author
CHECKED BY:	Checker
APPROVED BY:	Approver

#	DATE	DESCRIPTION

NOT FOR CONSTRUCTION

STAMP:

STAMP:

SHEET TITLE & NUMBER
LEVEL 02 FLOOR PLAN

A2.2.1

© 2018 Bluebeam, Inc.

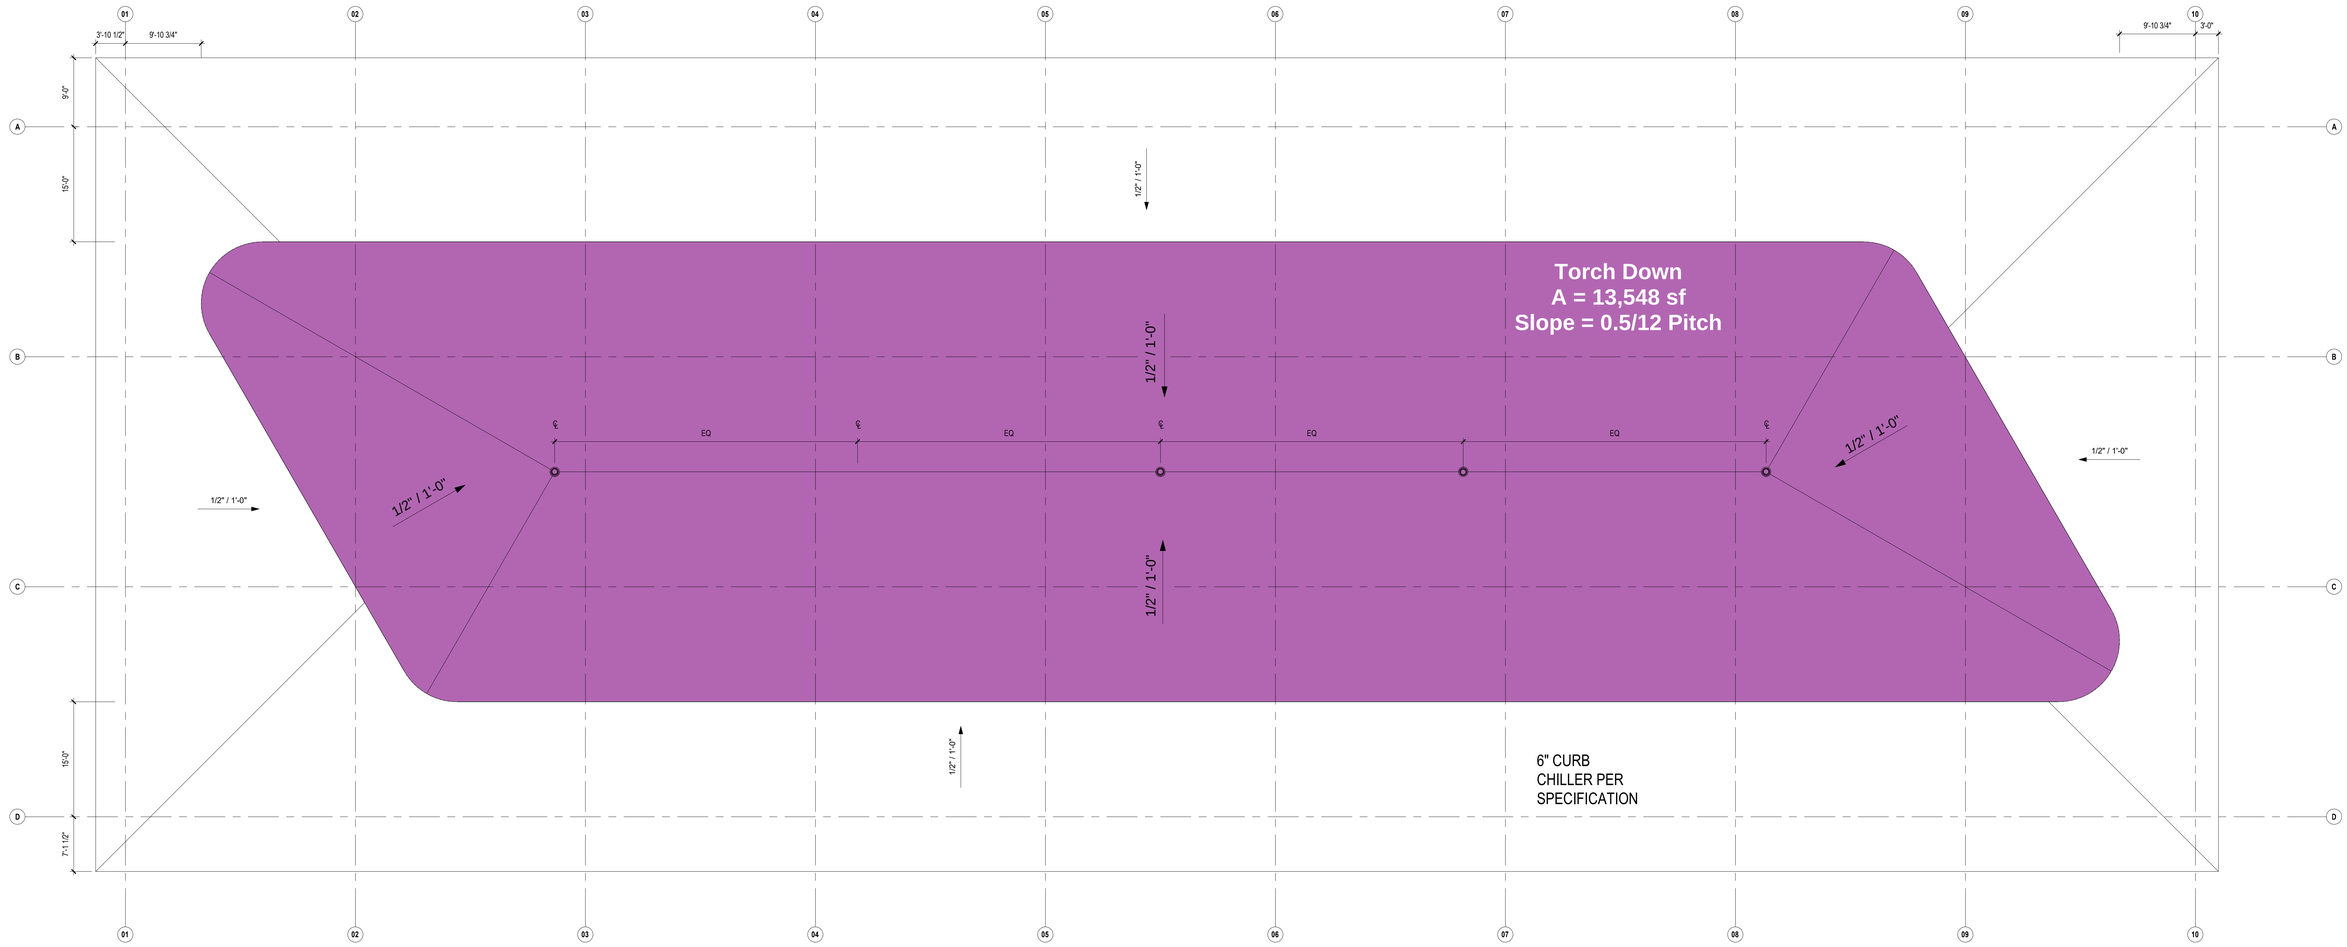

Level 07 1
SCALE: 1/8" = 1'-0"

BLUEBEAM®
A NEMETSCHEK COMPANY

CAPTURE ENGINEERS
Mechanical
Electrical
Plumbing

1234 Miller St.
Manchester, NH 06930

REVU ARCHITECTS

5555 N. Broad St
Pasadena CA 91101

OFFICE BUILDING

Project No: 323232

Project Address:
123 Schonsett St
Chicago, IL 60601

THIS DRAWING IS INTENDED FOR DEMONSTRATION PURPOSES ONLY. DO NOT USE THIS DRAWING FOR ANY OTHER PURPOSE WITHOUT THE EXPRESS WRITTEN PERMISSION OF BLUEBEAM, INC.

DATE	03/04/2018
ISSUED FOR:	INTERNAL REVIEW
PROJECT	3232
DRAWN BY:	Author
CHECKED BY:	Checker
APPROVED BY:	Approver

#	DATE	DESCRIPTION

NOT FOR CONSTRUCTION

STAMP:

STAMP:

SHEET TITLE & NUMBER
ROOF PLAN

A2.6.1

© 2018 Bluebeam, Inc.

Return Diffuser 80

Supply Diffuser 108

BLUEBEAM®
A NEMETSCHEK COMPANY

CAPTURE ENGINEERS
Mechanical
Electrical
Plumbing

1234 Miller St.
Manchester, NH 06930

REVU ARCHITECTS

5555 N. Broad St
Pasadena CA 91101

OFFICE BUILDING

Project No: 323232

Project Address:
123 Schonsett St
Chicago, IL 60601

THIS DRAWING IS INTENDED FOR DEMONSTRATION PURPOSES ONLY. DO NOT USE THIS DRAWING FOR ANY OTHER PURPOSE WITHOUT THE EXPRESS WRITTEN PERMISSION OF BLUEBEAM, INC.

DATE	03/04/2018
ISSUED FOR:	INTERNAL REVIEW
PROJECT	3232
DRAWN BY:	Author
CHECKED BY:	Checker
APPROVED BY:	Approver

#	DATE	DESCRIPTION

NOT FOR CONSTRUCTION

STAMP:

STAMP:

SHEET TITLE & NUMBER

LEVEL 02 REFLECTED CEILING PLAN

A2.2.3

© 2018 Bluebeam, Inc.

	Description	Quantity	Unit
	Cold Water	234.85	ft
	Hot Water	416.06	ft
	Sink 1	6	Count
	Storm Drain	186.37	ft
	Toilets	6	Count
	Waste	120.06	ft

BLUEBEAM®
A NEMETSCHEK COMPANY

CAPTURE ENGINEERS
Mechanical
Electrical
Plumbing

1234 Miller St.
Manchester, NH 06930

REVU ARCHITECTS

5555 N. Broad St
Pasadena CA 91101

OFFICE BUILDING

Project No: 323232

Project Address:
123 Schonsett St
Chicago, IL 60601

THIS DRAWING IS INTENDED FOR DEMONSTRATION PURPOSES ONLY. DO NOT USE THIS DRAWING FOR ANY OTHER PURPOSE WITHOUT THE EXPRESS WRITTEN PERMISSION OF BLUEBEAM, INC.

DATE	03/04/2018
ISSUED FOR:	INTERNAL REVIEW
PROJECT	3232
DRAWN BY:	Author
CHECKED BY:	Checker
APPROVED BY:	Approver

#	DATE	DESCRIPTION

NOT FOR CONSTRUCTION

STAMP:

STAMP:

SHEET TITLE & NUMBER
PLUMBING - LEVEL 2

P2.02

© 2018 Bluebeam, Inc.

12"x12"	43.46	ft
18"x12"	64.22	ft
20"x14"	38.68	ft
24"x16"	156.92	ft
28"x18"	59.9416	ft
30"x16"	68.88	ft
36"x30"	199.38	ft
VAV	26	Count

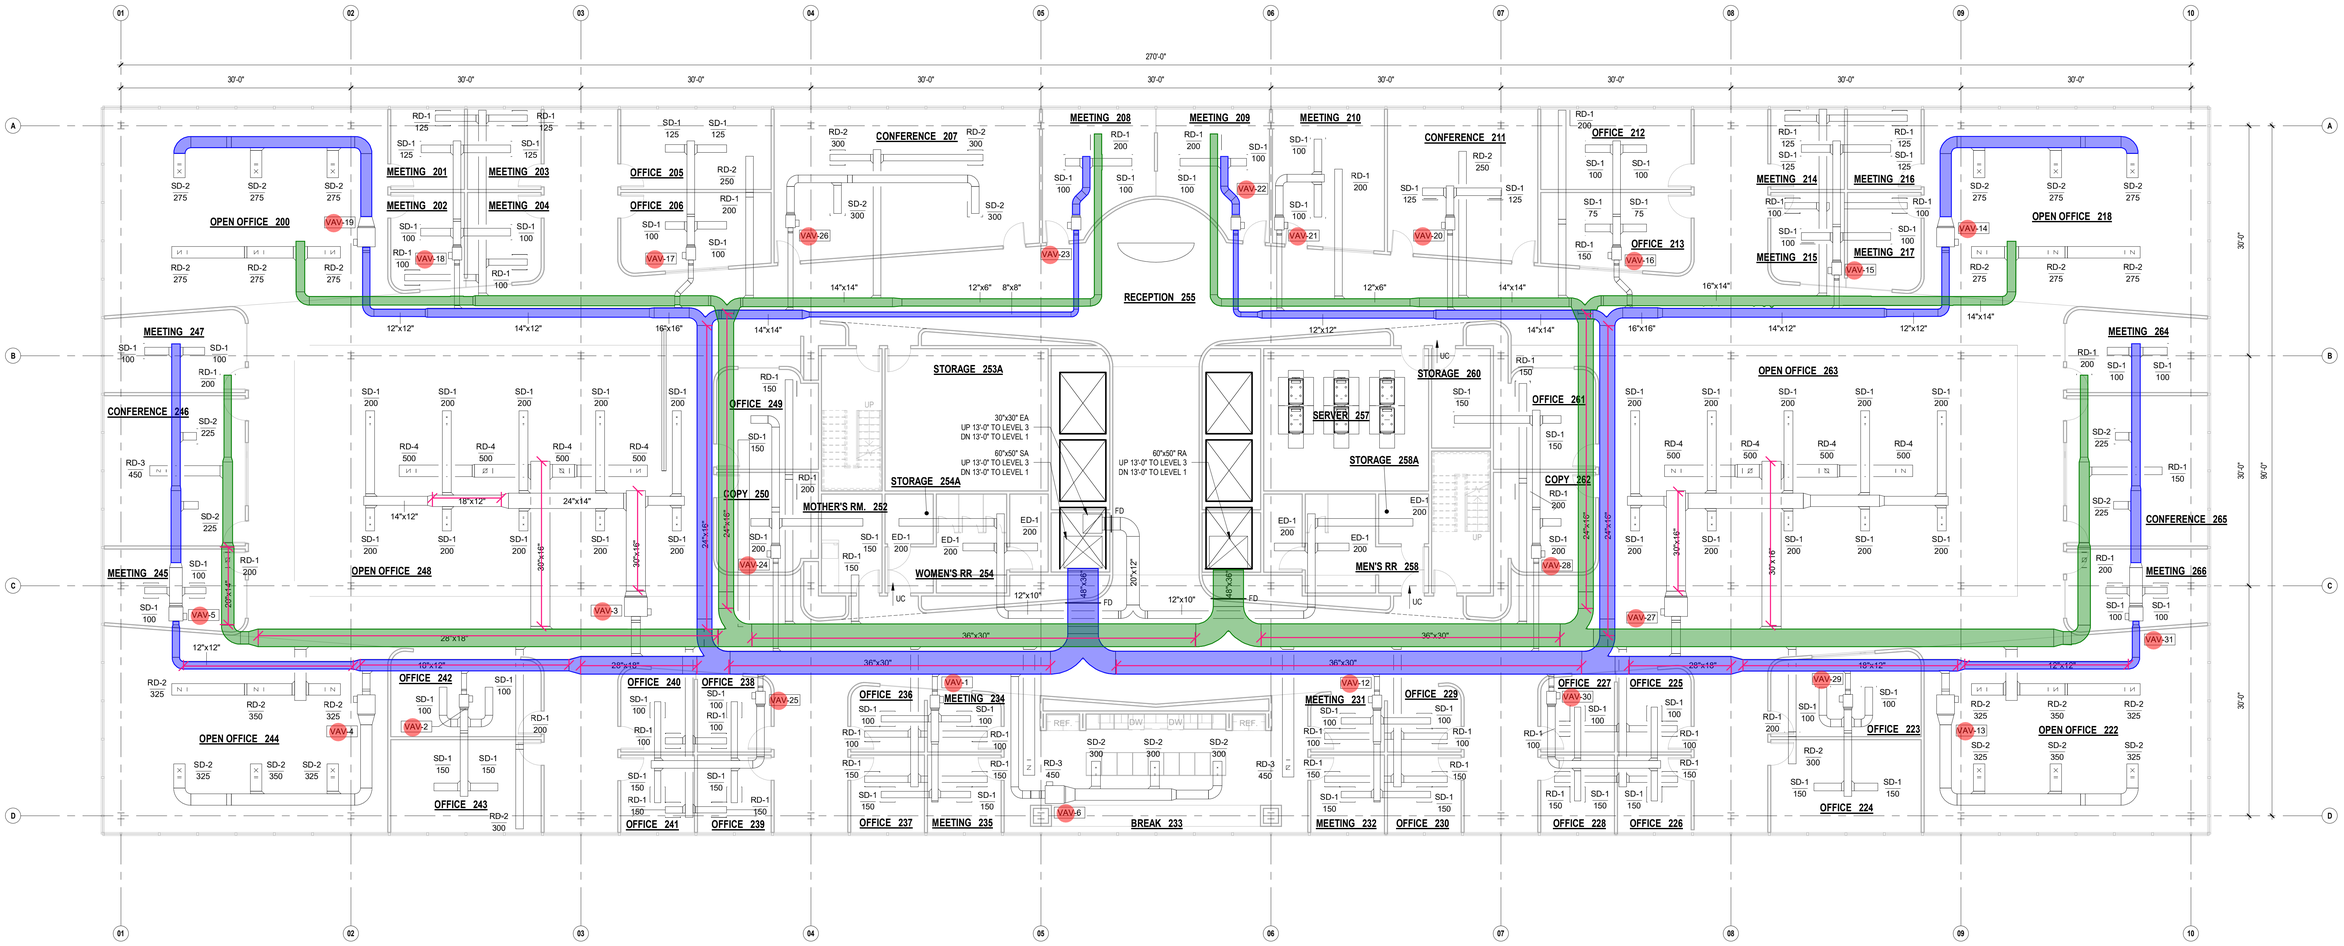

Level 02 HVAC 2
SCALE: 1/8" = 1'-0"

BLUEBEAM®
A NEMETSCHEK COMPANY

CAPTURE ENGINEERS
Mechanical
Electrical
Plumbing

1234 Miller St.
Manchester, NH 06930

REVU ARCHITECTS

5555 N. Broad St
Pasadena CA 91101

OFFICE BUILDING

Project No: 323232

Project Address:
123 Schonsett St
Chicago, IL 60601

THIS DRAWING IS INTENDED FOR DEMONSTRATION PURPOSES ONLY. DO NOT USE THIS DRAWING FOR ANY OTHER PURPOSE WITHOUT THE EXPRESS WRITTEN PERMISSION OF BLUEBEAM, INC.

DATE	03/04/2018
ISSUED FOR:	INTERNAL REVIEW
PROJECT	3232
DRAWN BY:	Author
CHECKED BY:	Checker
APPROVED BY:	Approver

#	DATE	DESCRIPTION

NOT FOR CONSTRUCTION

STAMP:

STAMP:

SHEET TITLE & NUMBER
MECHANICAL LAYOUT - LEVEL 2

M2.02

© 2018 Bluebeam, Inc.

ELECTRICAL

3/4" EMT Conduit	499.29	ft
Quad Receptacle	18	Count

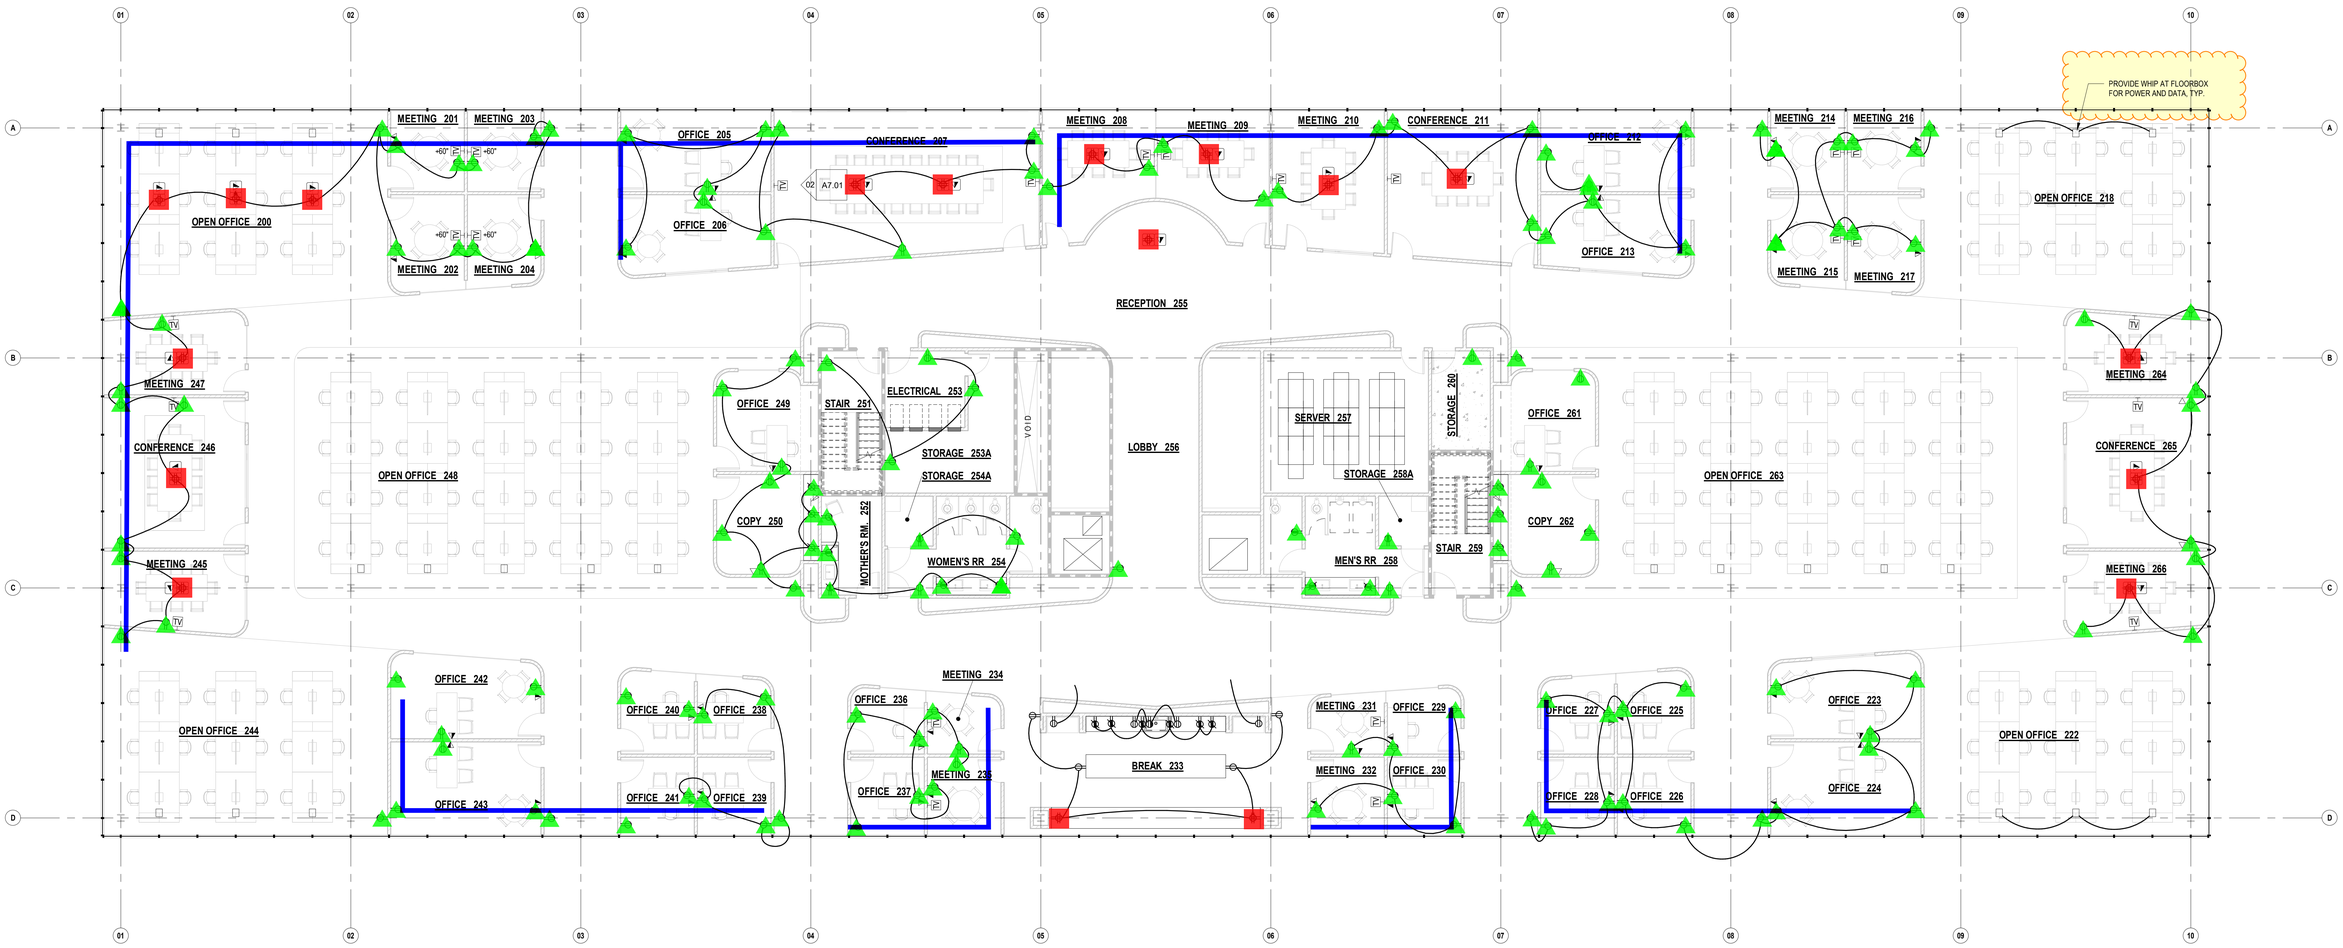

BLUEBEAM®
A NEMETSCHEK COMPANY

CAPTURE ENGINEERS
Mechanical
Electrical
Plumbing

1234 Miller St.
Manchester, NH 06930

REVU ARCHITECTS

5555 N. Broad St
Pasadena CA 91101

OFFICE BUILDING

Project No: 323232

Project Address:
123 Schonsett St
Chicago, IL 60601

THIS DRAWING IS INTENDED FOR DEMONSTRATION PURPOSES ONLY. DO NOT USE THIS DRAWING FOR ANY OTHER PURPOSE WITHOUT THE EXPRESS WRITTEN PERMISSION OF BLUEBEAM, INC.

DATE	03/04/2018
ISSUED FOR:	INTERNAL REVIEW
PROJECT	3232
DRAWN BY:	Author
CHECKED BY:	Checker
APPROVED BY:	Approver

#	DATE	DESCRIPTION

NOT FOR CONSTRUCTION

STAMP:

STAMP:

SHEET TITLE & NUMBER
ELECTRICAL PLAN - LEVEL 2

E2.02

© 2018 Bluebeam, Inc.

Description	Label	Quantity	Unit
4" Sidewalk	3500 PSI Concrete	32,525	sf
Resurfacing	Asphalt	103,331	sf

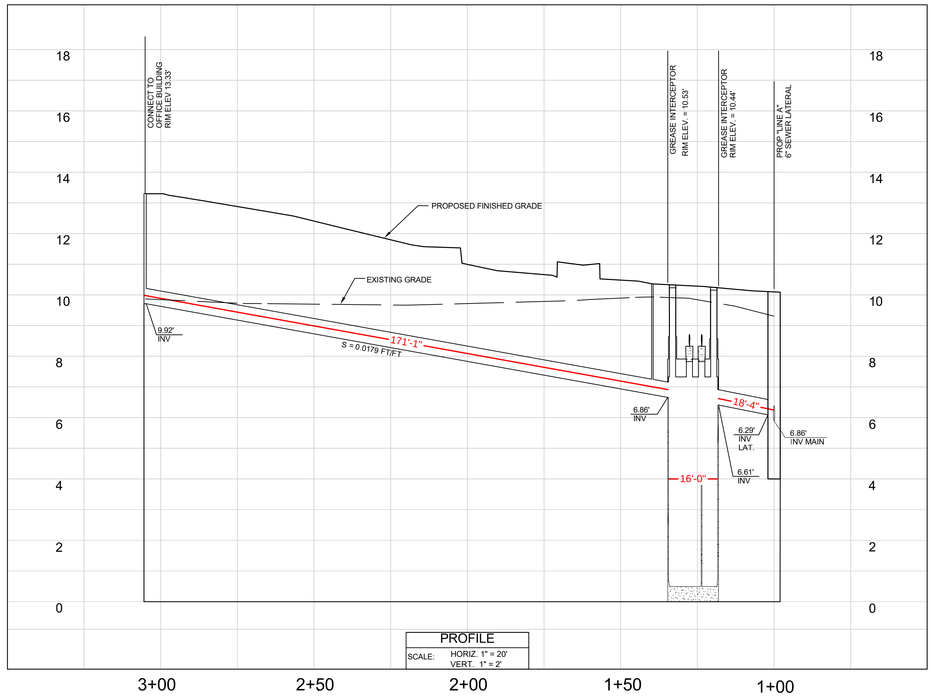

PROFILE 2

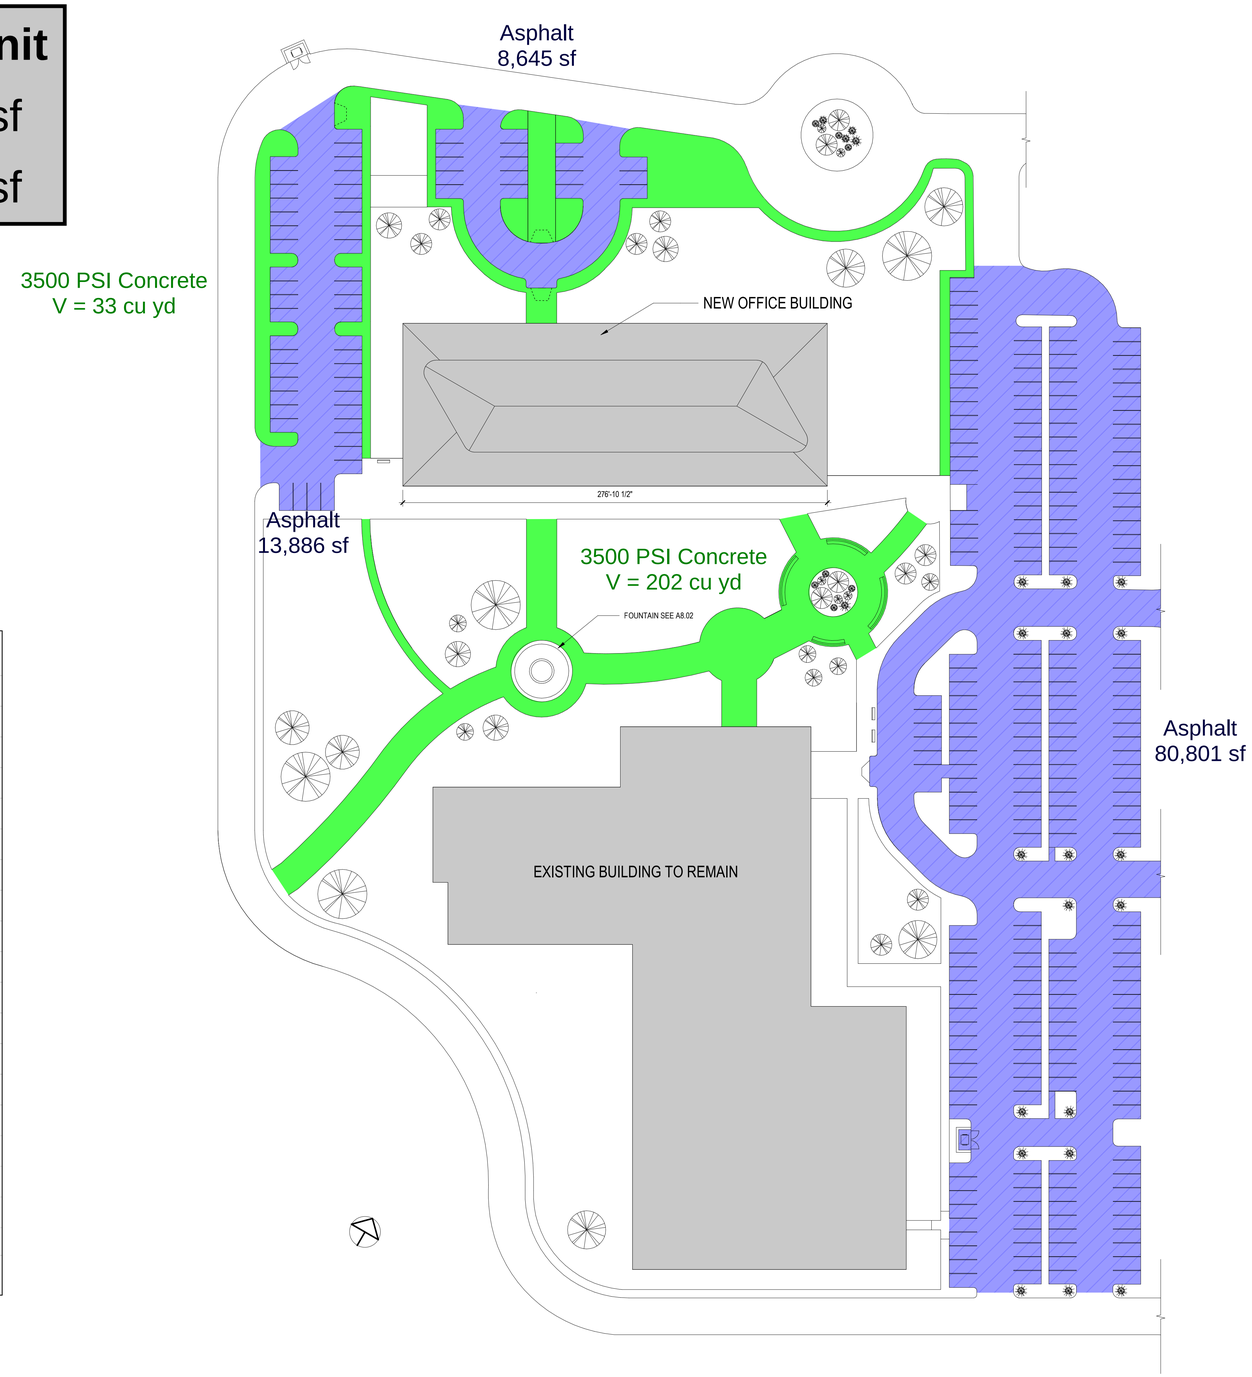

Site Plan 1
SCALE: 1" = 40'-0"

BLUEBEAM®
A NEMETSCHEK COMPANY

CAPTURE ENGINEERS
Mechanical
Electrical
Plumbing

1234 Miller St.
Manchester, NH 06930

REVU ARCHITECTS

5555 N. Broad St
Pasadena CA 91101

OFFICE BUILDING

Project No: 323232

Project Address:
123 Schonsett St
Chicago, IL 60601

THIS DRAWING IS INTENDED FOR DEMONSTRATION PURPOSES ONLY. DO NOT USE THIS DRAWING FOR ANY OTHER PURPOSE WITHOUT THE EXPRESS WRITTEN PERMISSION OF BLUEBEAM, INC.

DATE	03/04/2018
ISSUED FOR:	INTERNAL REVIEW
PROJECT	3232
DRAWN BY:	Author
CHECKED BY:	Checker
APPROVED BY:	Approver

#	DATE	DESCRIPTION

NOT FOR CONSTRUCTION

STAMP:

STAMP:

SHEET TITLE & NUMBER
SITE PLAN

A1.01

© 2018 Bluebeam, Inc.

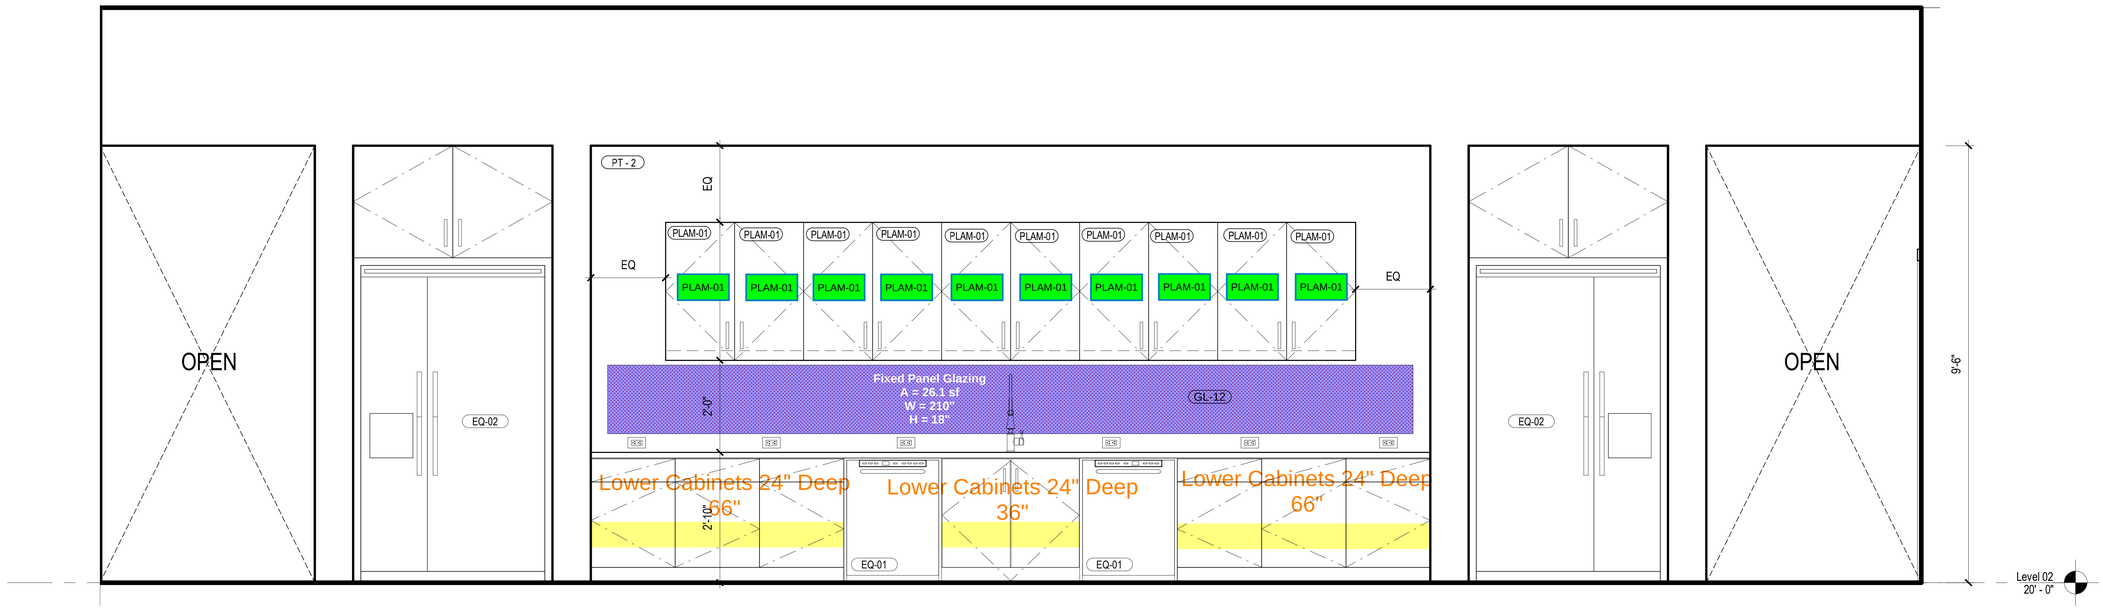

ELEVATION 1 - BREAK ROOM 233 01

SCALE: 1/2" = 1'-0"

BLUEBEAM®
A NEMETSCHEK COMPANY

CAPTURE ENGINEERS
Mechanical
Electrical
Plumbing

1234 Miller St.
Manchester, NH 06930

REVU ARCHITECTS

5555 N. Broad St
Pasadena CA 91101

OFFICE BUILDING

Project No: 323232

Project Address:
123 Schonsett St
Chicago, IL 60601

THIS DRAWING IS INTENDED FOR DEMONSTRATION PURPOSES ONLY. DO NOT USE THIS DRAWING FOR ANY OTHER PURPOSE WITHOUT THE EXPRESS WRITTEN PERMISSION OF BLUEBEAM, INC.

DATE	03/04/2018
ISSUED FOR:	INTERNAL REVIEW
PROJECT	3232
DRAWN BY:	Author
CHECKED BY:	Checker
APPROVED BY:	Approver

#	DATE	DESCRIPTION

NOT FOR CONSTRUCTION

STAMP:

STAMP:

SHEET TITLE & NUMBER
INTERIOR ELEVATIONS

A7.01

© 2018 Bluebeam, Inc.